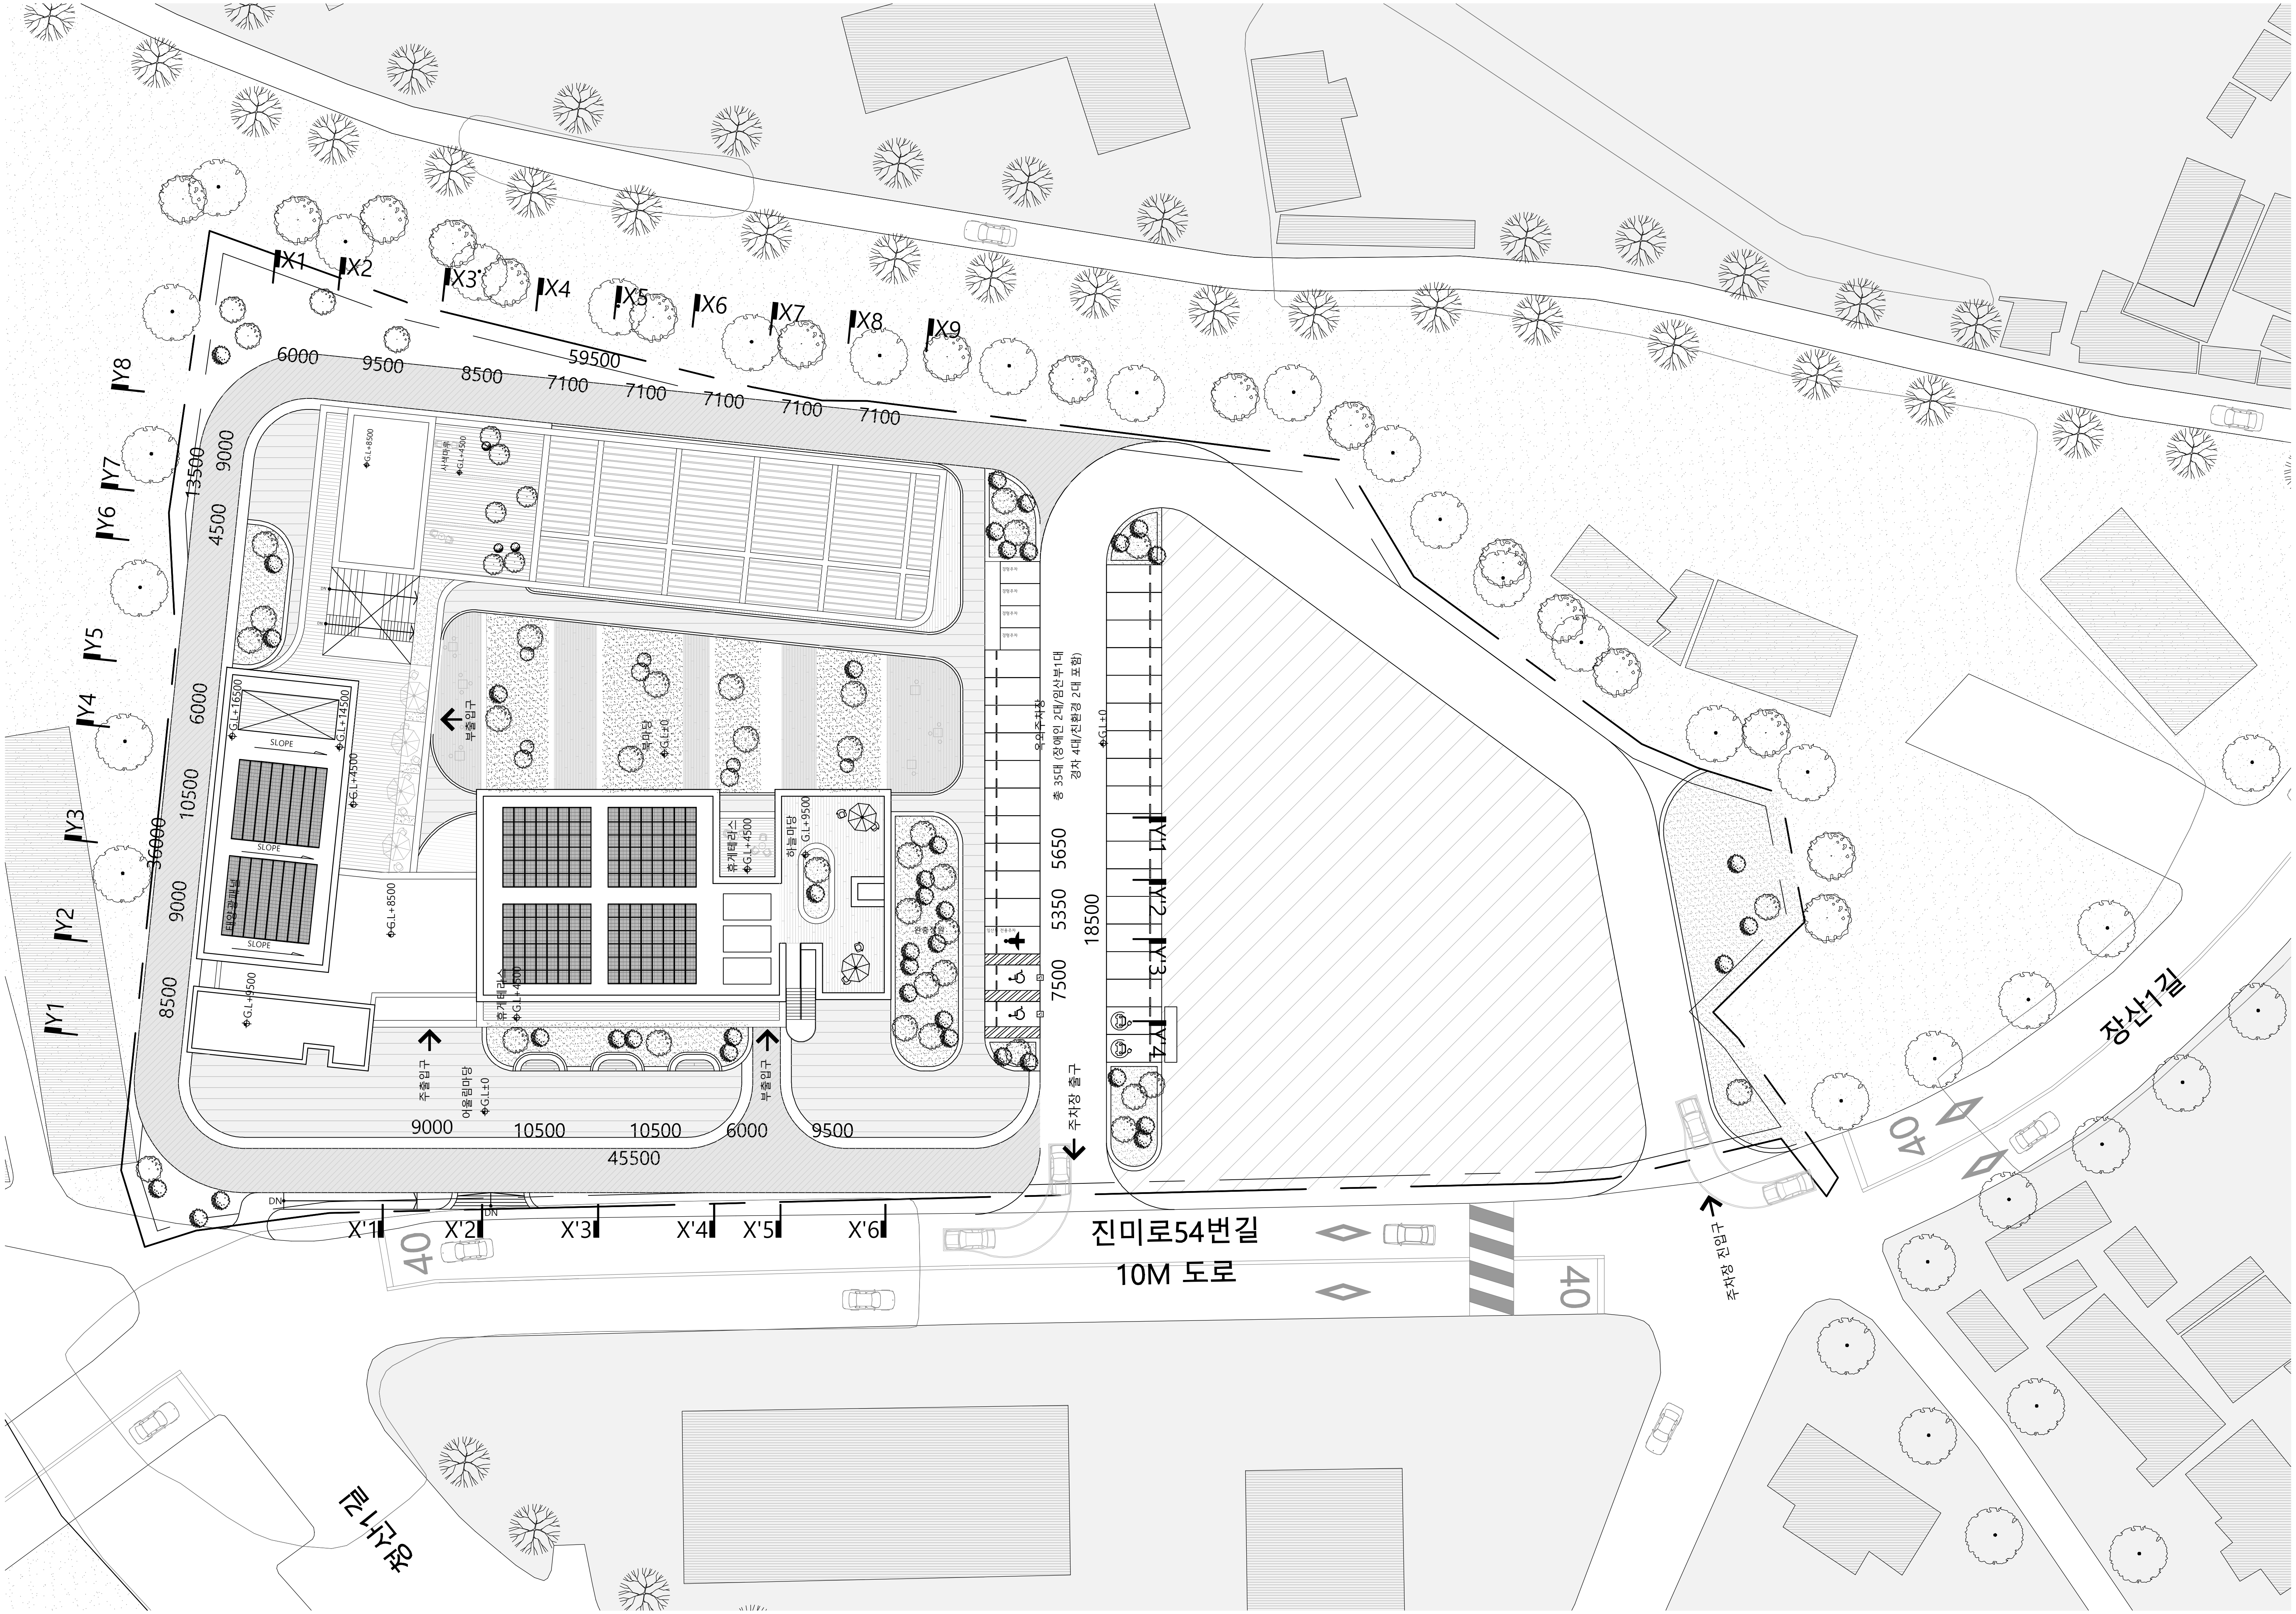
X1
X2
X3
X4
X5
X6
X7
X8
X9
59500
6000
9500
8500
7100
7100
7100
7100
7100
Y8
Y7
Y6
Y5
Y4
Y3
Y2
Y1
13500
9000
4500
6000
10500
36000
9000
8500
G.L+16500
G.L+14500
SLOPE
SLOPE
SLOPE
태양광패널
G.L+4500
G.L+8500
G.L+9500
G.L+8500
사색마루
G.L+4500
부출입구
북마당
G.L±0
휴게테라스
G.L+4500
하늘마당
G.L+9500
휴게테라스
G.L+4500
완충정원
주출입구
어울림마당
G.L±0
부출입구
9000
10500
10500
6000
9500
45500
경형주차
경형주차
경형주차
경형주차
옥외주차장
총 35대 (장애인 2대/임산부1대
경차 4대/친환경 2대 포함)
G.L±0
임산부 전용주차
5650
5350
7500
18500
Y'1
Y'2
Y'3
Y'4
주차장 출구
DN
DN
X'1
X'2
X'3
X'4
X'5
X'6
40
40
40
40
진미로54번길
10M 도로
주차장 진입구
장산1길
장산2길