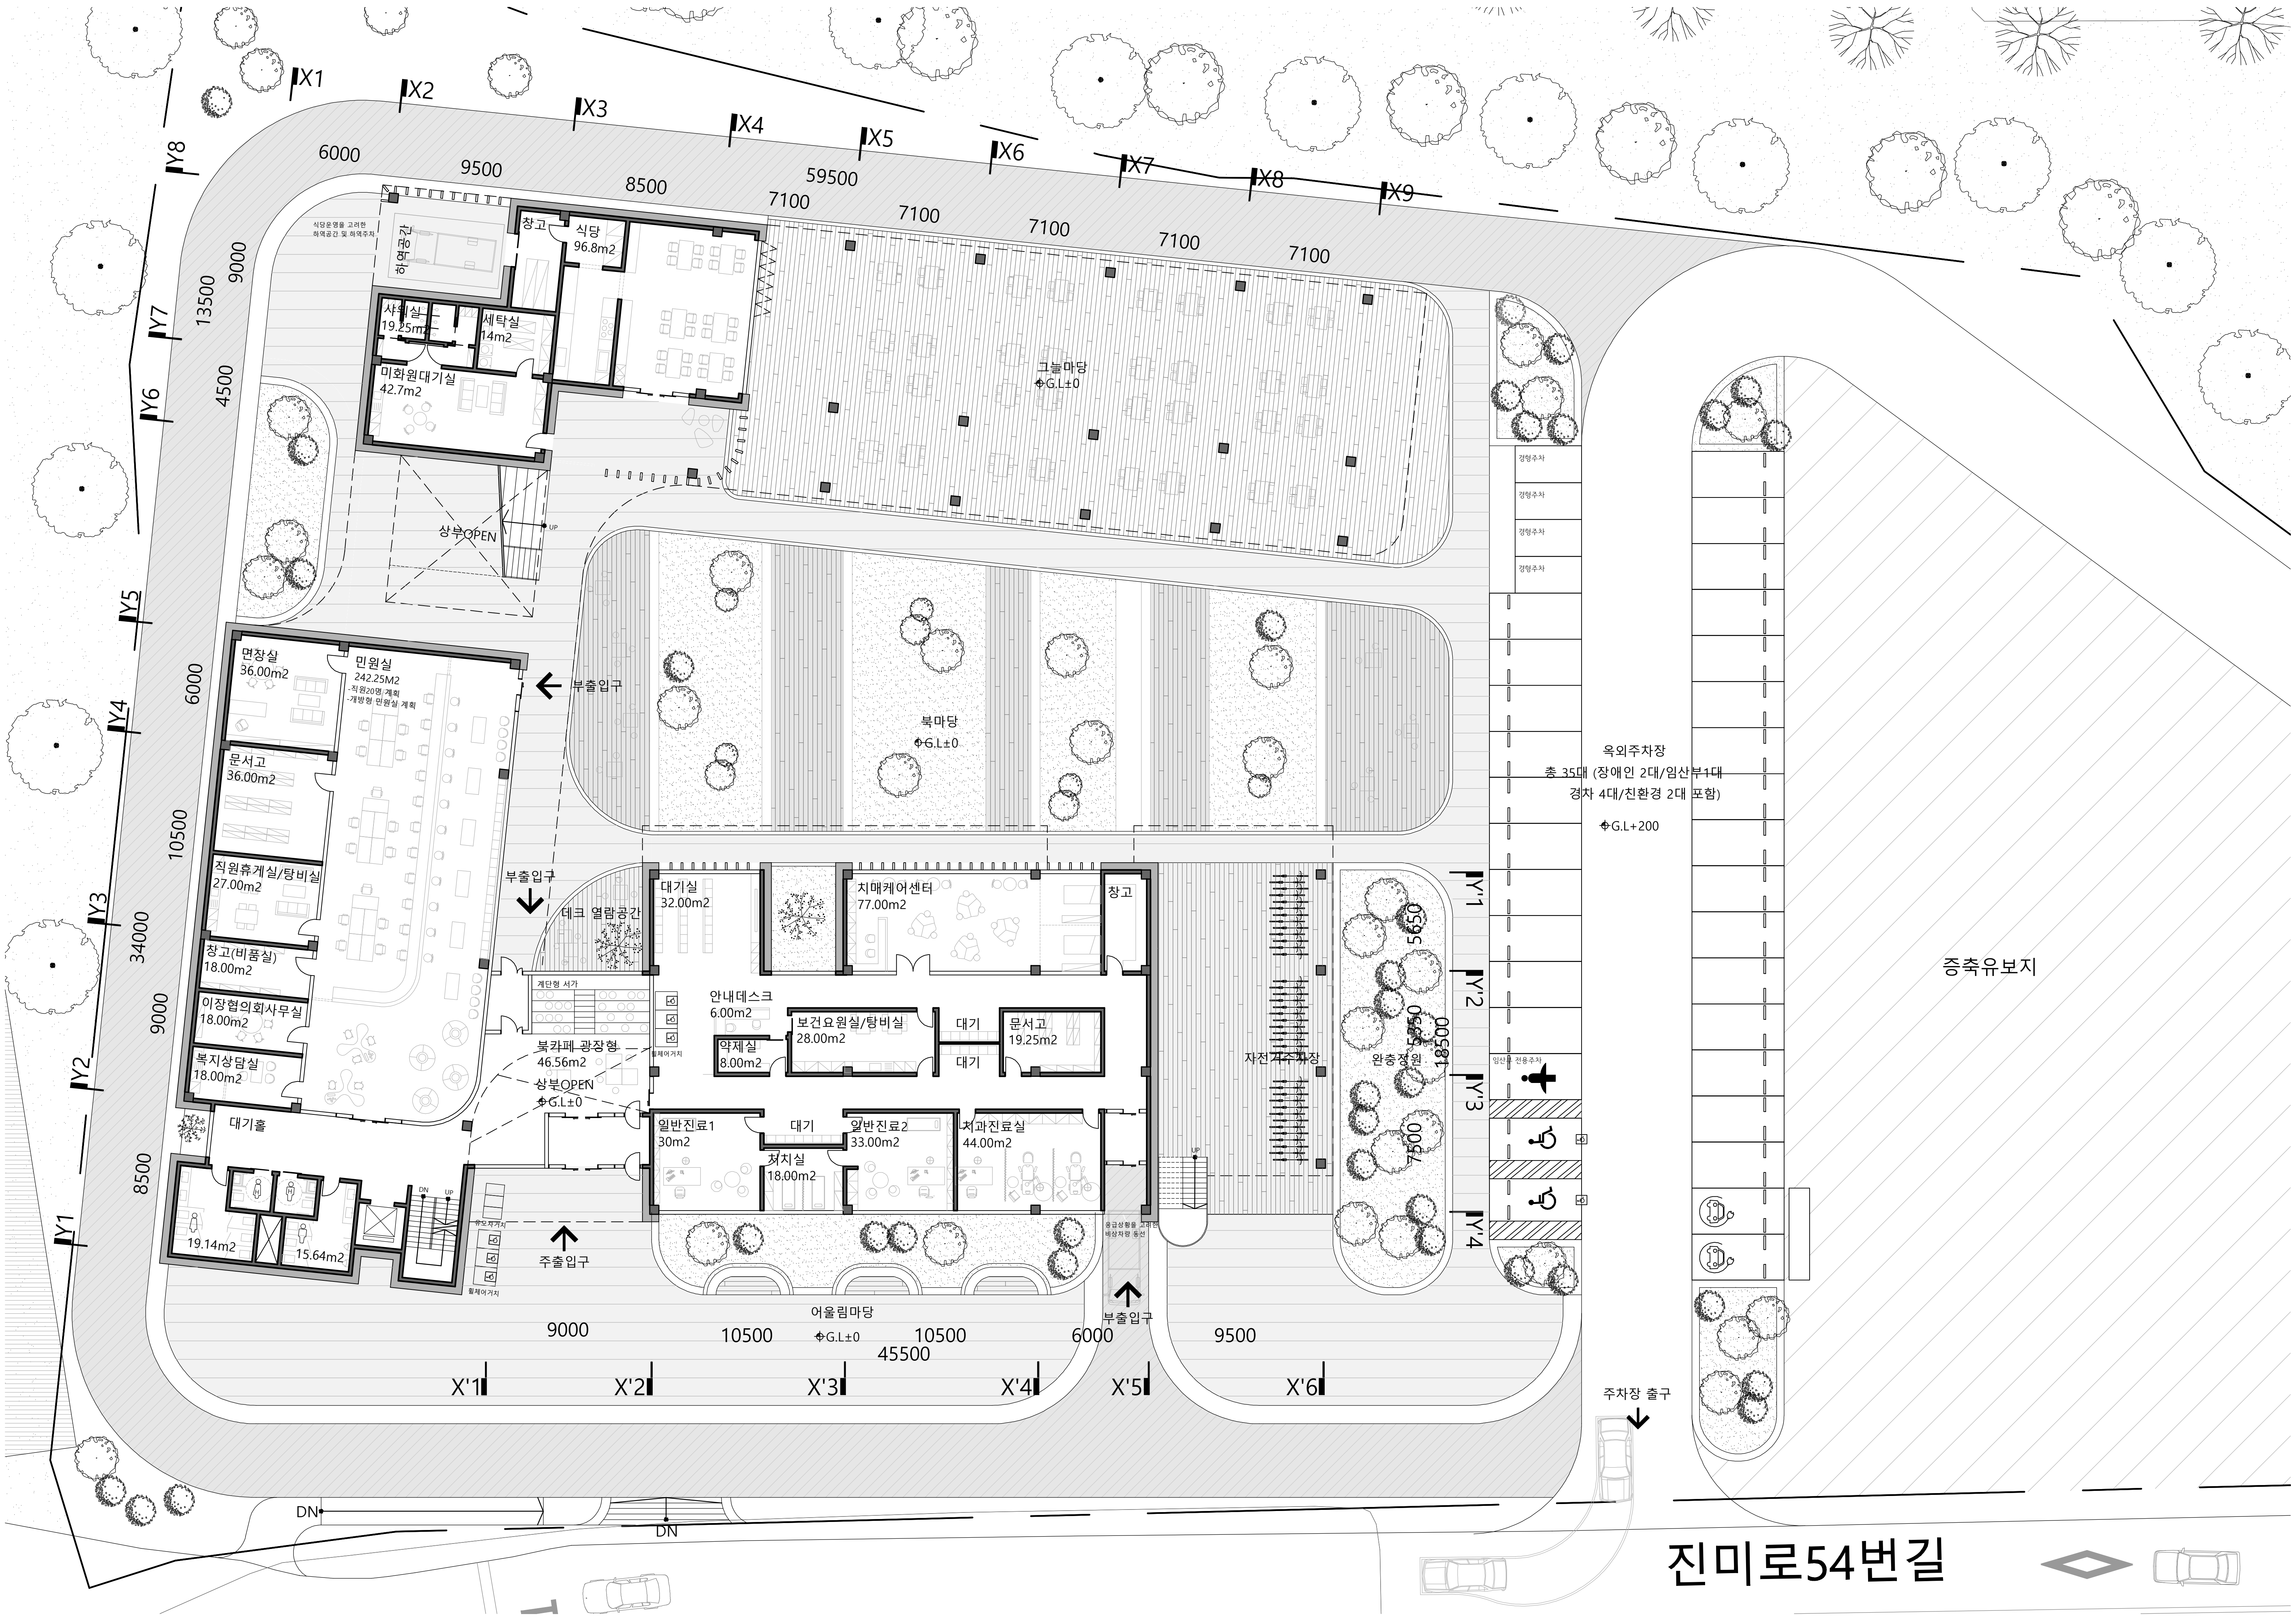
X1
X2
X3
X4
X5
X6
X7
X8
X9
6000
9500
8500
59500
7100
7100
7100
7100
7100
Y8
Y7
Y6
Y5
Y4
Y3
Y2
Y1
9000
13500
4500
6000
10500
34000
9000
8500
식당운영을 고려한
하역공간 및 하역주차
하역공간
창고
식당
96.8m2
샤워실
19.25m2
세탁실
14m2
미화원대기실
42.7m2
상부OPEN
UP
그늘마당
G.L±0
경형주차
경형주차
경형주차
경형주차
면장실
36.00m2
민원실
242.25M2
-직원20명 계획
-개방형 민원실 계획
부출입구
문서고
36.00m2
직원휴게실/탕비실
27.00m2
창고(비품실)
18.00m2
이장협의회사무실
18.00m2
복지상담실
18.00m2
대기홀
19.14m2
15.64m2
DN
UP
유모차거치
휠체어거치
주출입구
부출입구
데크 열람공간
계단형 서가
휠체어거치
북카페 광장형
46.56m2
상부OPEN
G.L±0
북마당
G.L±0
대기실
32.00m2
치매케어센터
77.00m2
창고
안내데스크
6.00m2
보건요원실/탕비실
28.00m2
대기
문서고
19.25m2
약제실
8.00m2
대기
일반진료1
30m2
대기
처치실
18.00m2
일반진료2
33.00m2
치과진료실
44.00m2
응급상황을 고려한
비상차량 동선
부출입구
UP
자전거주차장
완충정원
Y'1
Y'2
Y'3
Y'4
5650
5350
7500
18500
옥외주차장
총 35대 (장애인 2대/임산부1대
경차 4대/친환경 2대 포함)
G.L+200
임산부 전용주차
증축유보지
어울림마당
G.L±0
9000
10500
10500
6000
9500
45500
X'1
X'2
X'3
X'4
X'5
X'6
주차장 출구
DN
DN
진미로54번길