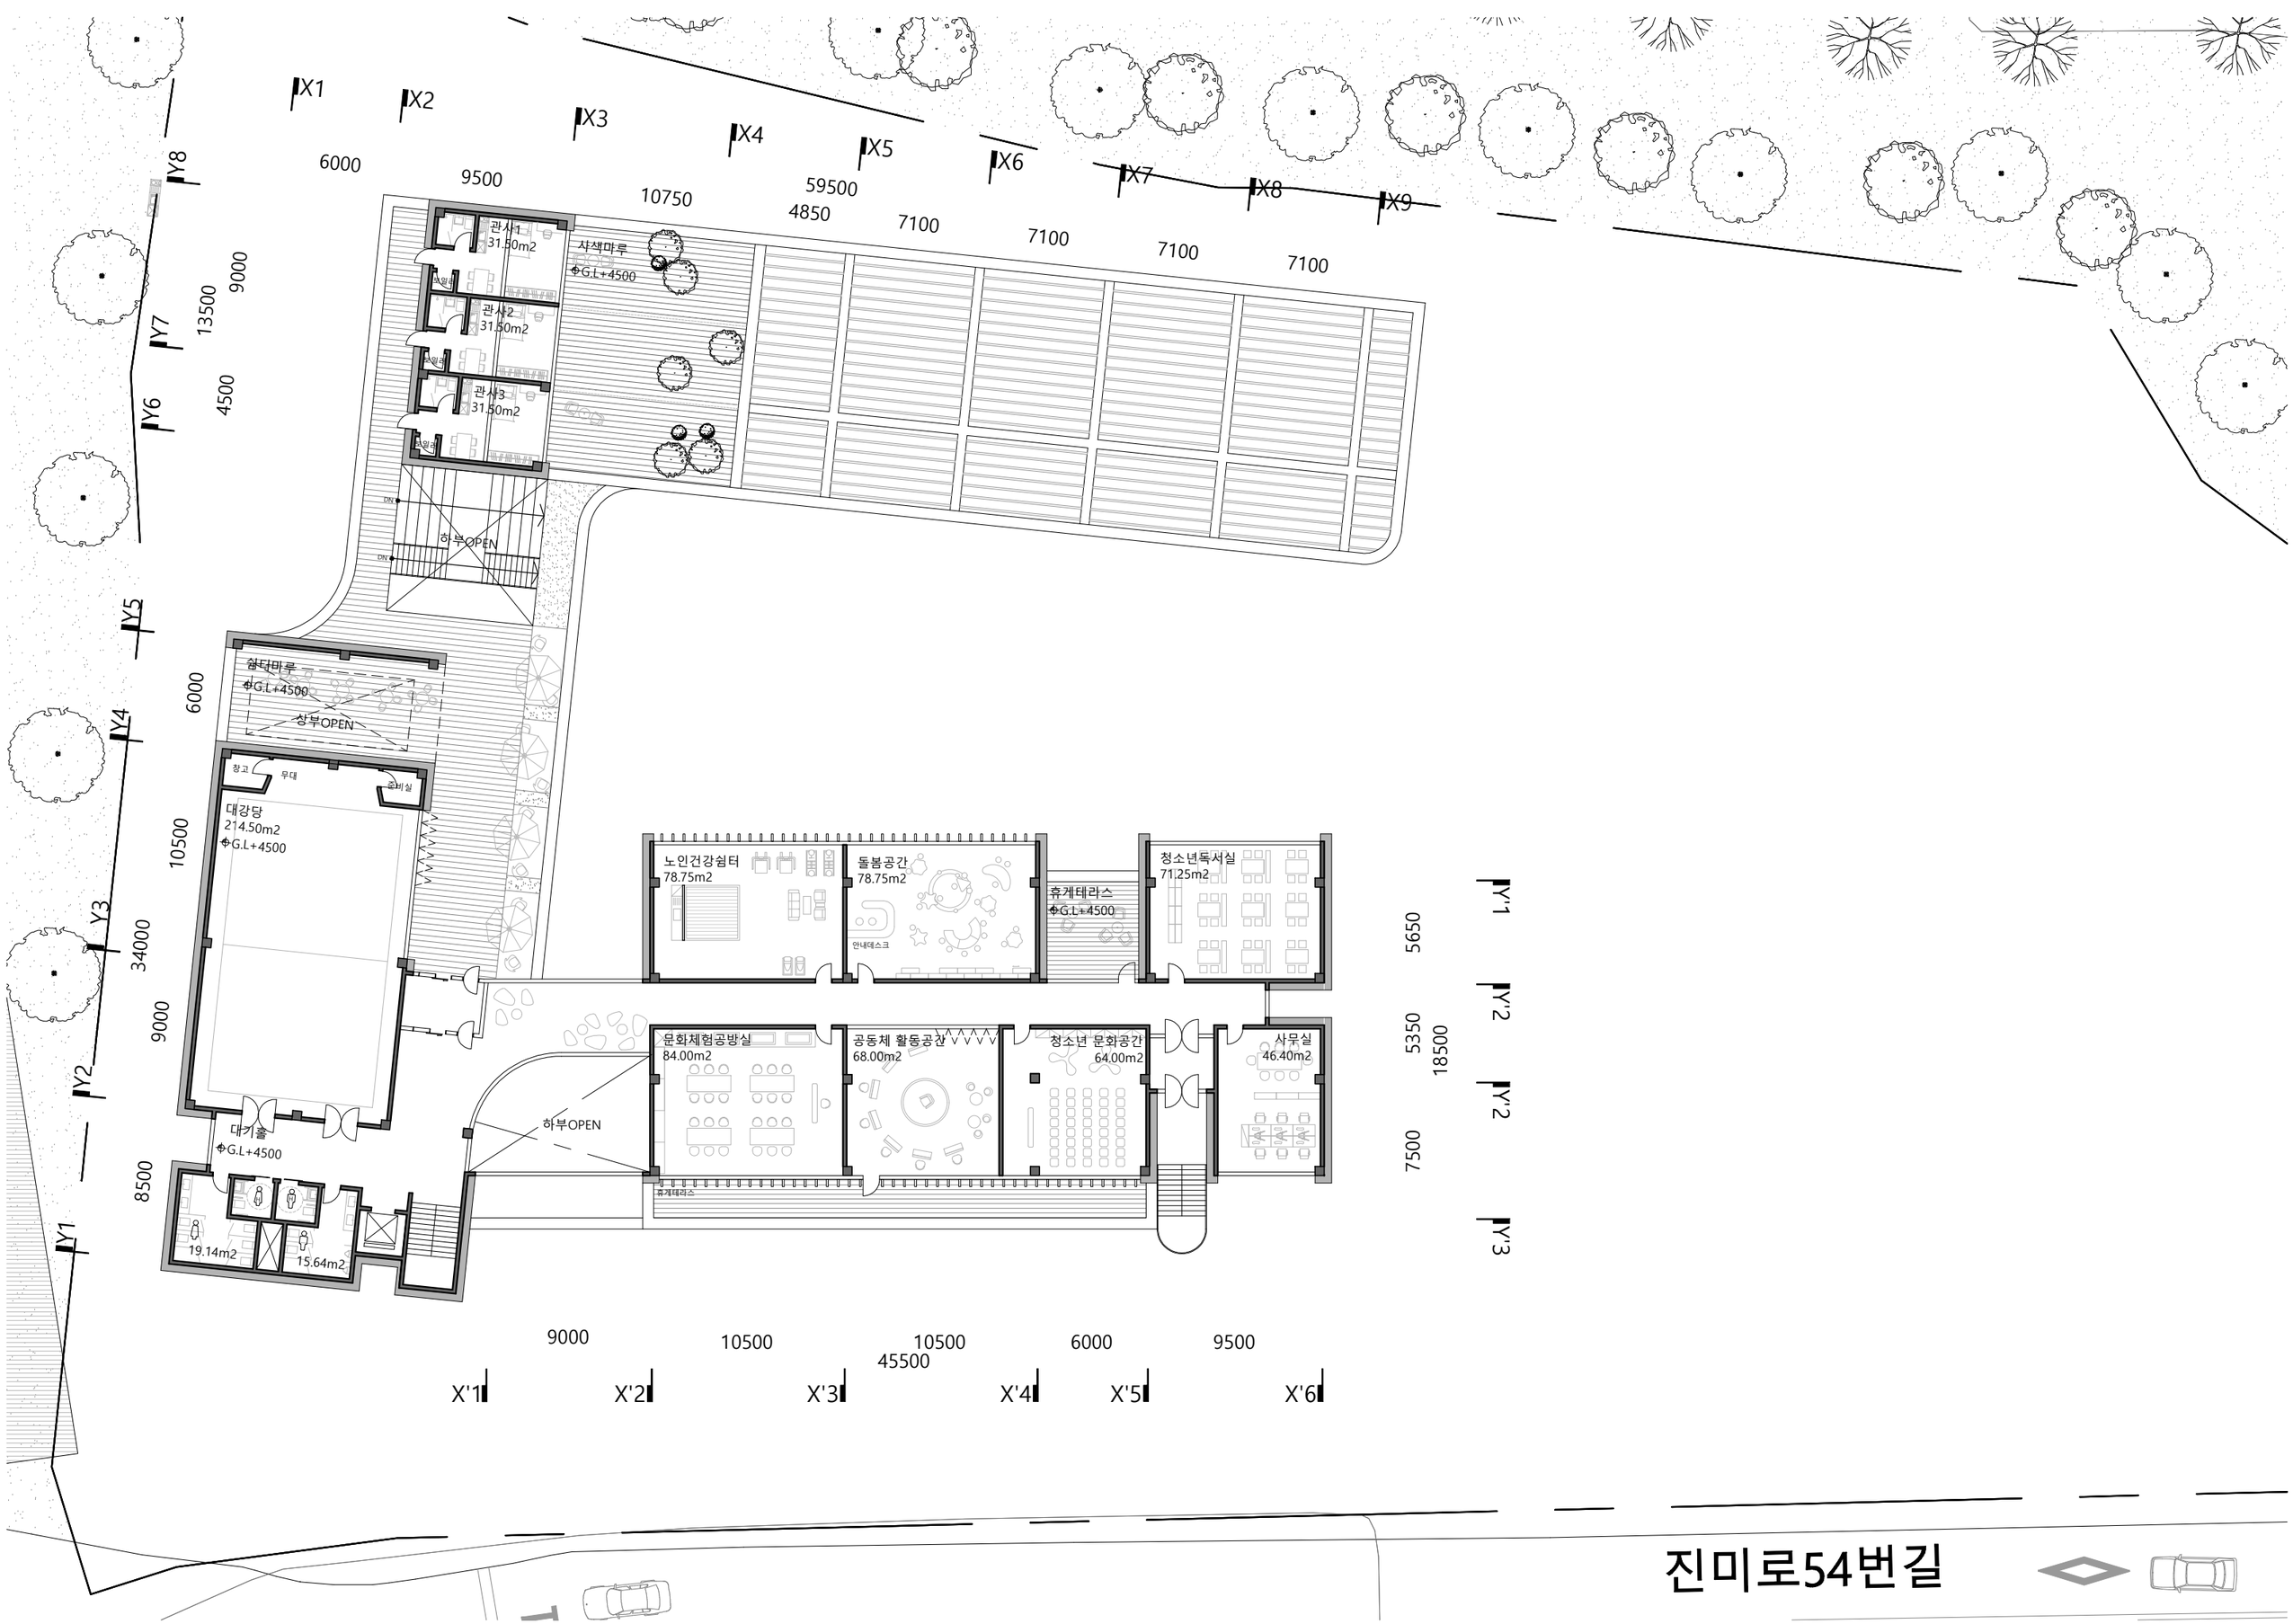

X1
X2
X3
X4
X5
X6
X7
X8
X9
Y8
Y7
Y6
Y5
Y4
Y3
Y2
Y1
6000
9500
10750
59500
4850
7100
7100
7100
7100
9000
13500
4500
6000
10500
34000
9000
8500
관사1
31.50m2
관사2
31.50m2
관사3
31.50m2
사색마루
G.L+4500
하부OPEN
참다미루
G.L+4500
상부OPEN
창고
무대
준비실
대강당
214.50m2
G.L+4500
대기홀
G.L+4500
19.14m2
15.64m2
노인건강쉼터
78.75m2
돌봄공간
78.75m2
안내데스크
휴게테라스
G.L+4500
청소년독서실
71.25m2
문화체험공방실
84.00m2
공동체 활동공간
68.00m2
청소년 문화공간
64.00m2
사무실
46.40m2
하부OPEN
휴게테라스
9000
10500
10500
6000
9500
45500
X'1
X'2
X'3
X'4
X'5
X'6
Y'1
Y'2
Y'2
Y'3
5650
5350
18500
7500
진미로54번길