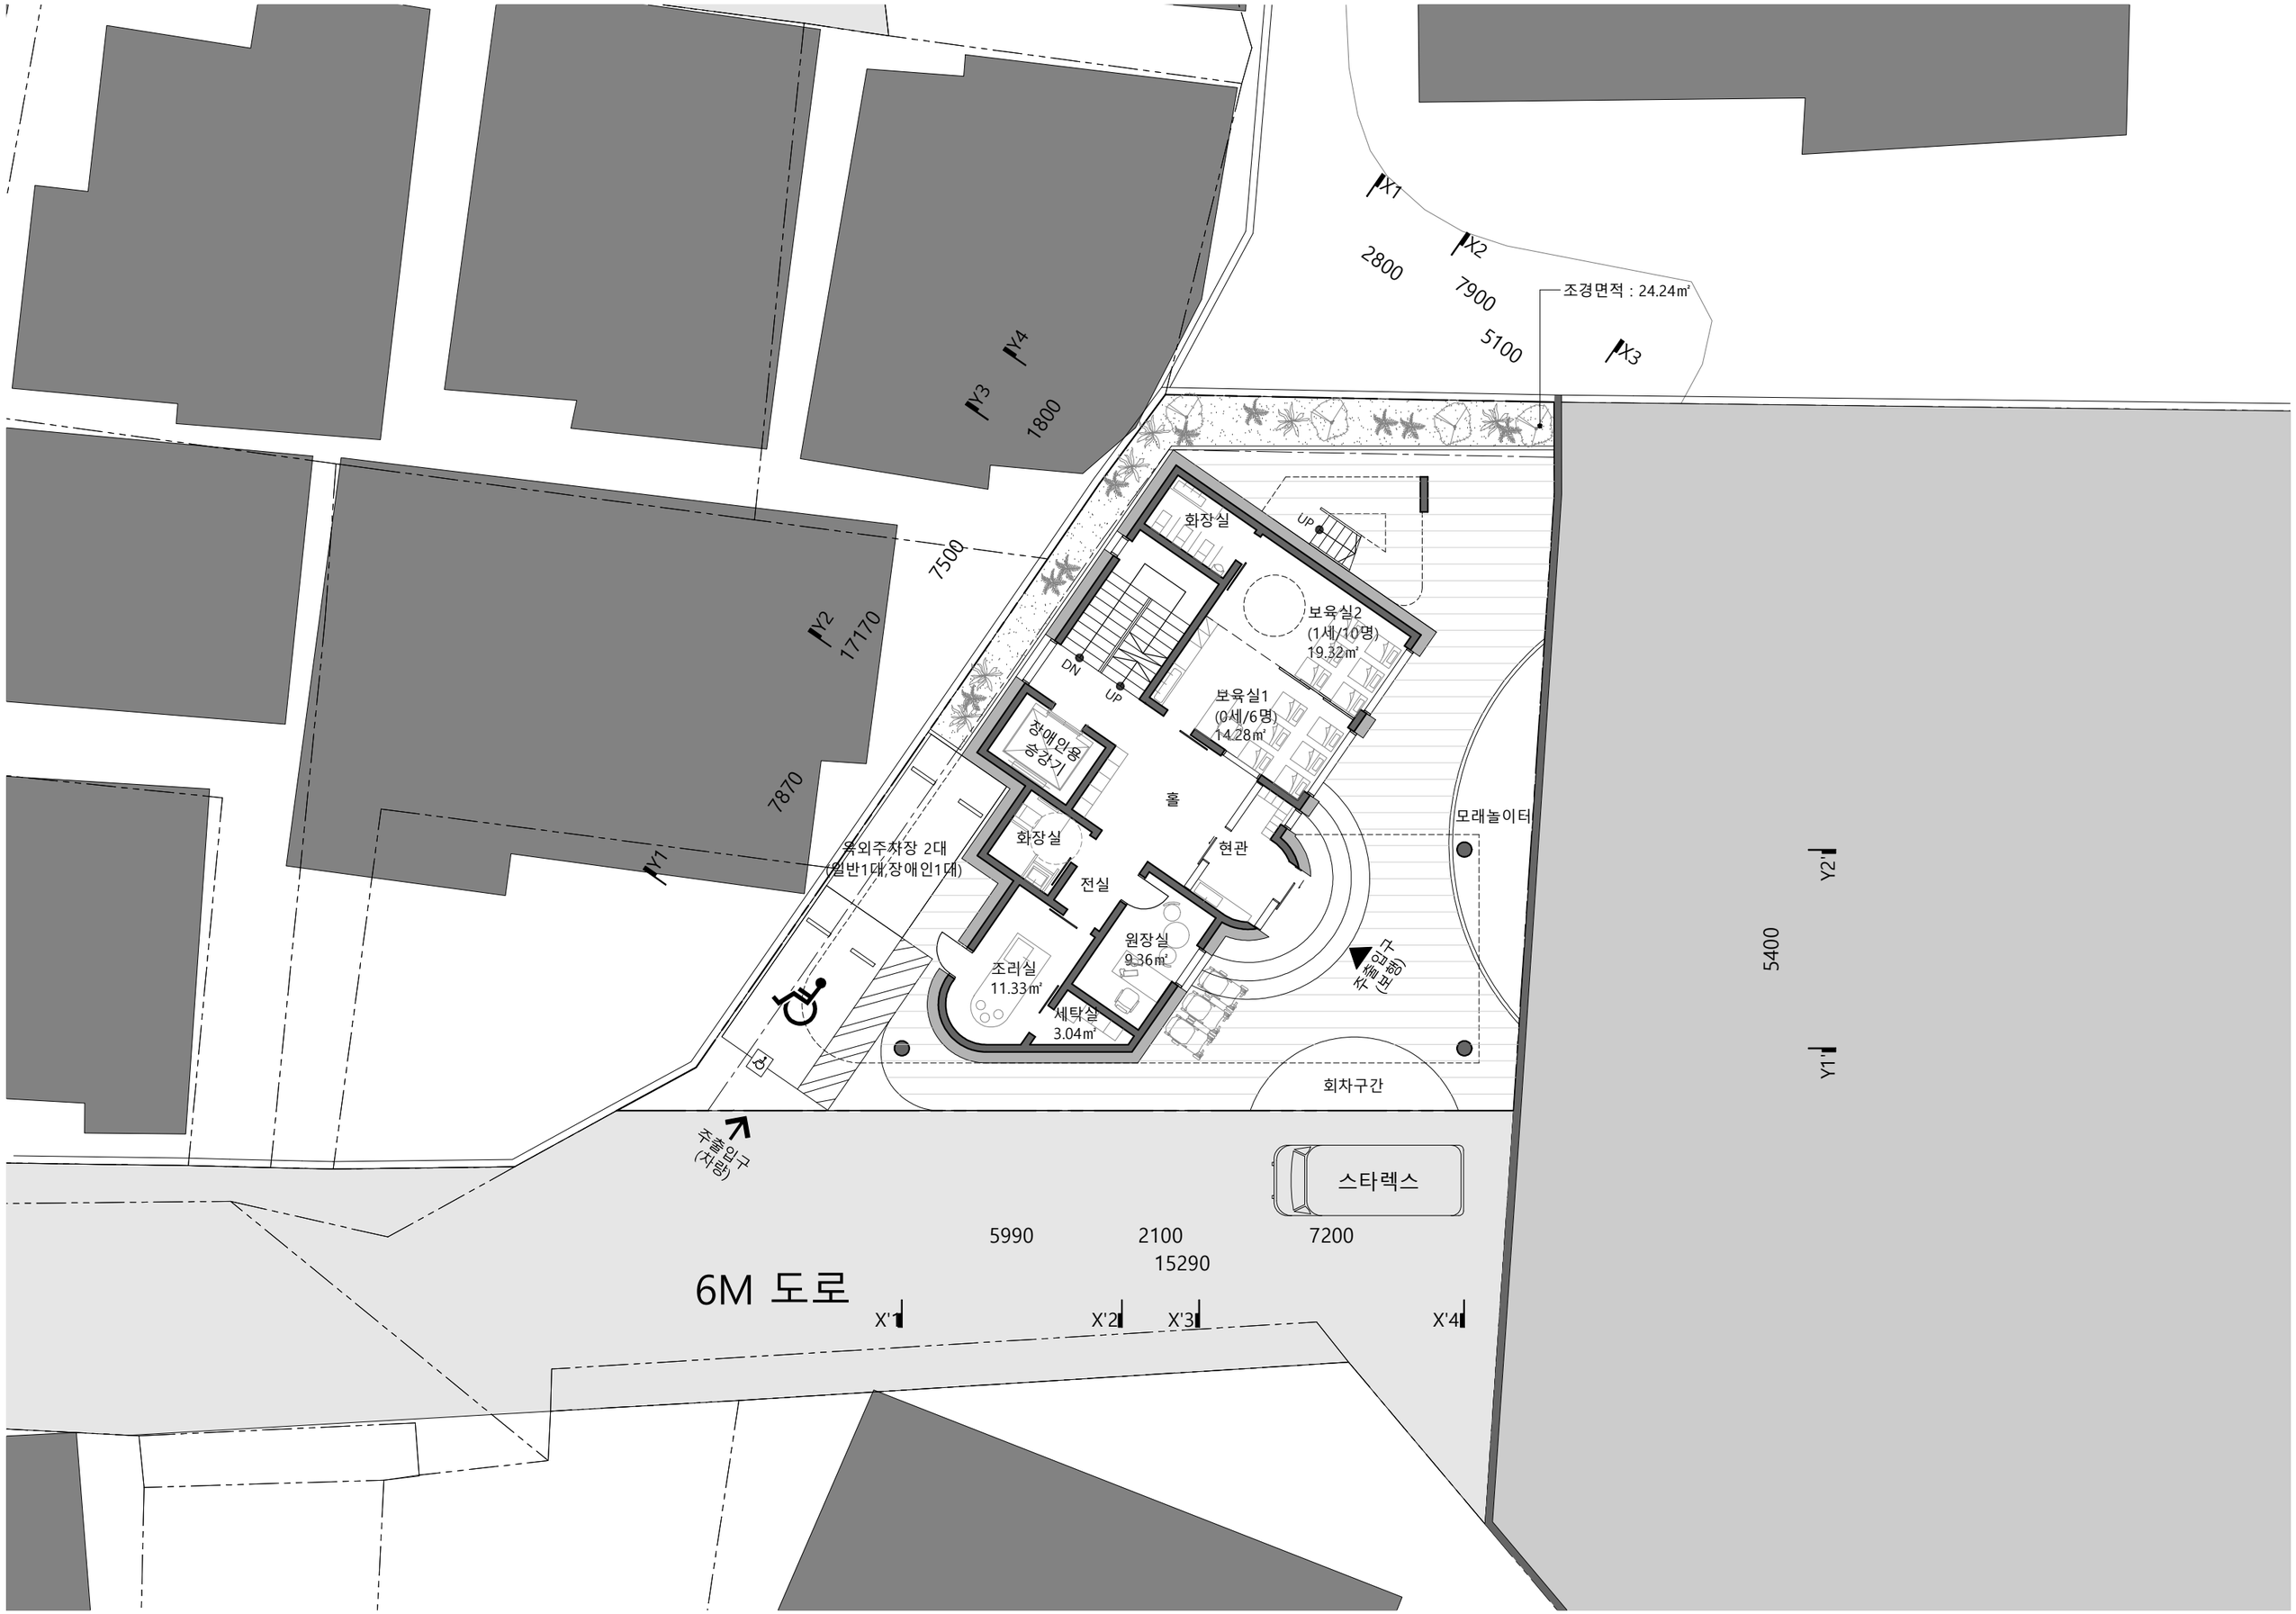

X1
X2
X3
X4
Y1
Y2
Y3
Y4
2800
7900
5100
1800
조경면적 : 24.24㎡
7500
17170
7870
화장실
UP
보육실2
(1세/10명)
19.32㎡
DN
UP
보육실1
(0세/6명)
14.28㎡
장애인용
승강기
홀
화장실
현관
전실
원장실
9.36㎡
조리실
11.33㎡
세탁실
3.04㎡
모래놀이터
주출입구
(보행자)
옥외주차장 2대
(일반1대,장애인1대)
회차구간
주출입구
(차량)
스타렉스
5990
2100
7200
15290
6M 도로
X'1
X'2
X'3
X'4
Y'1
Y'2
5400