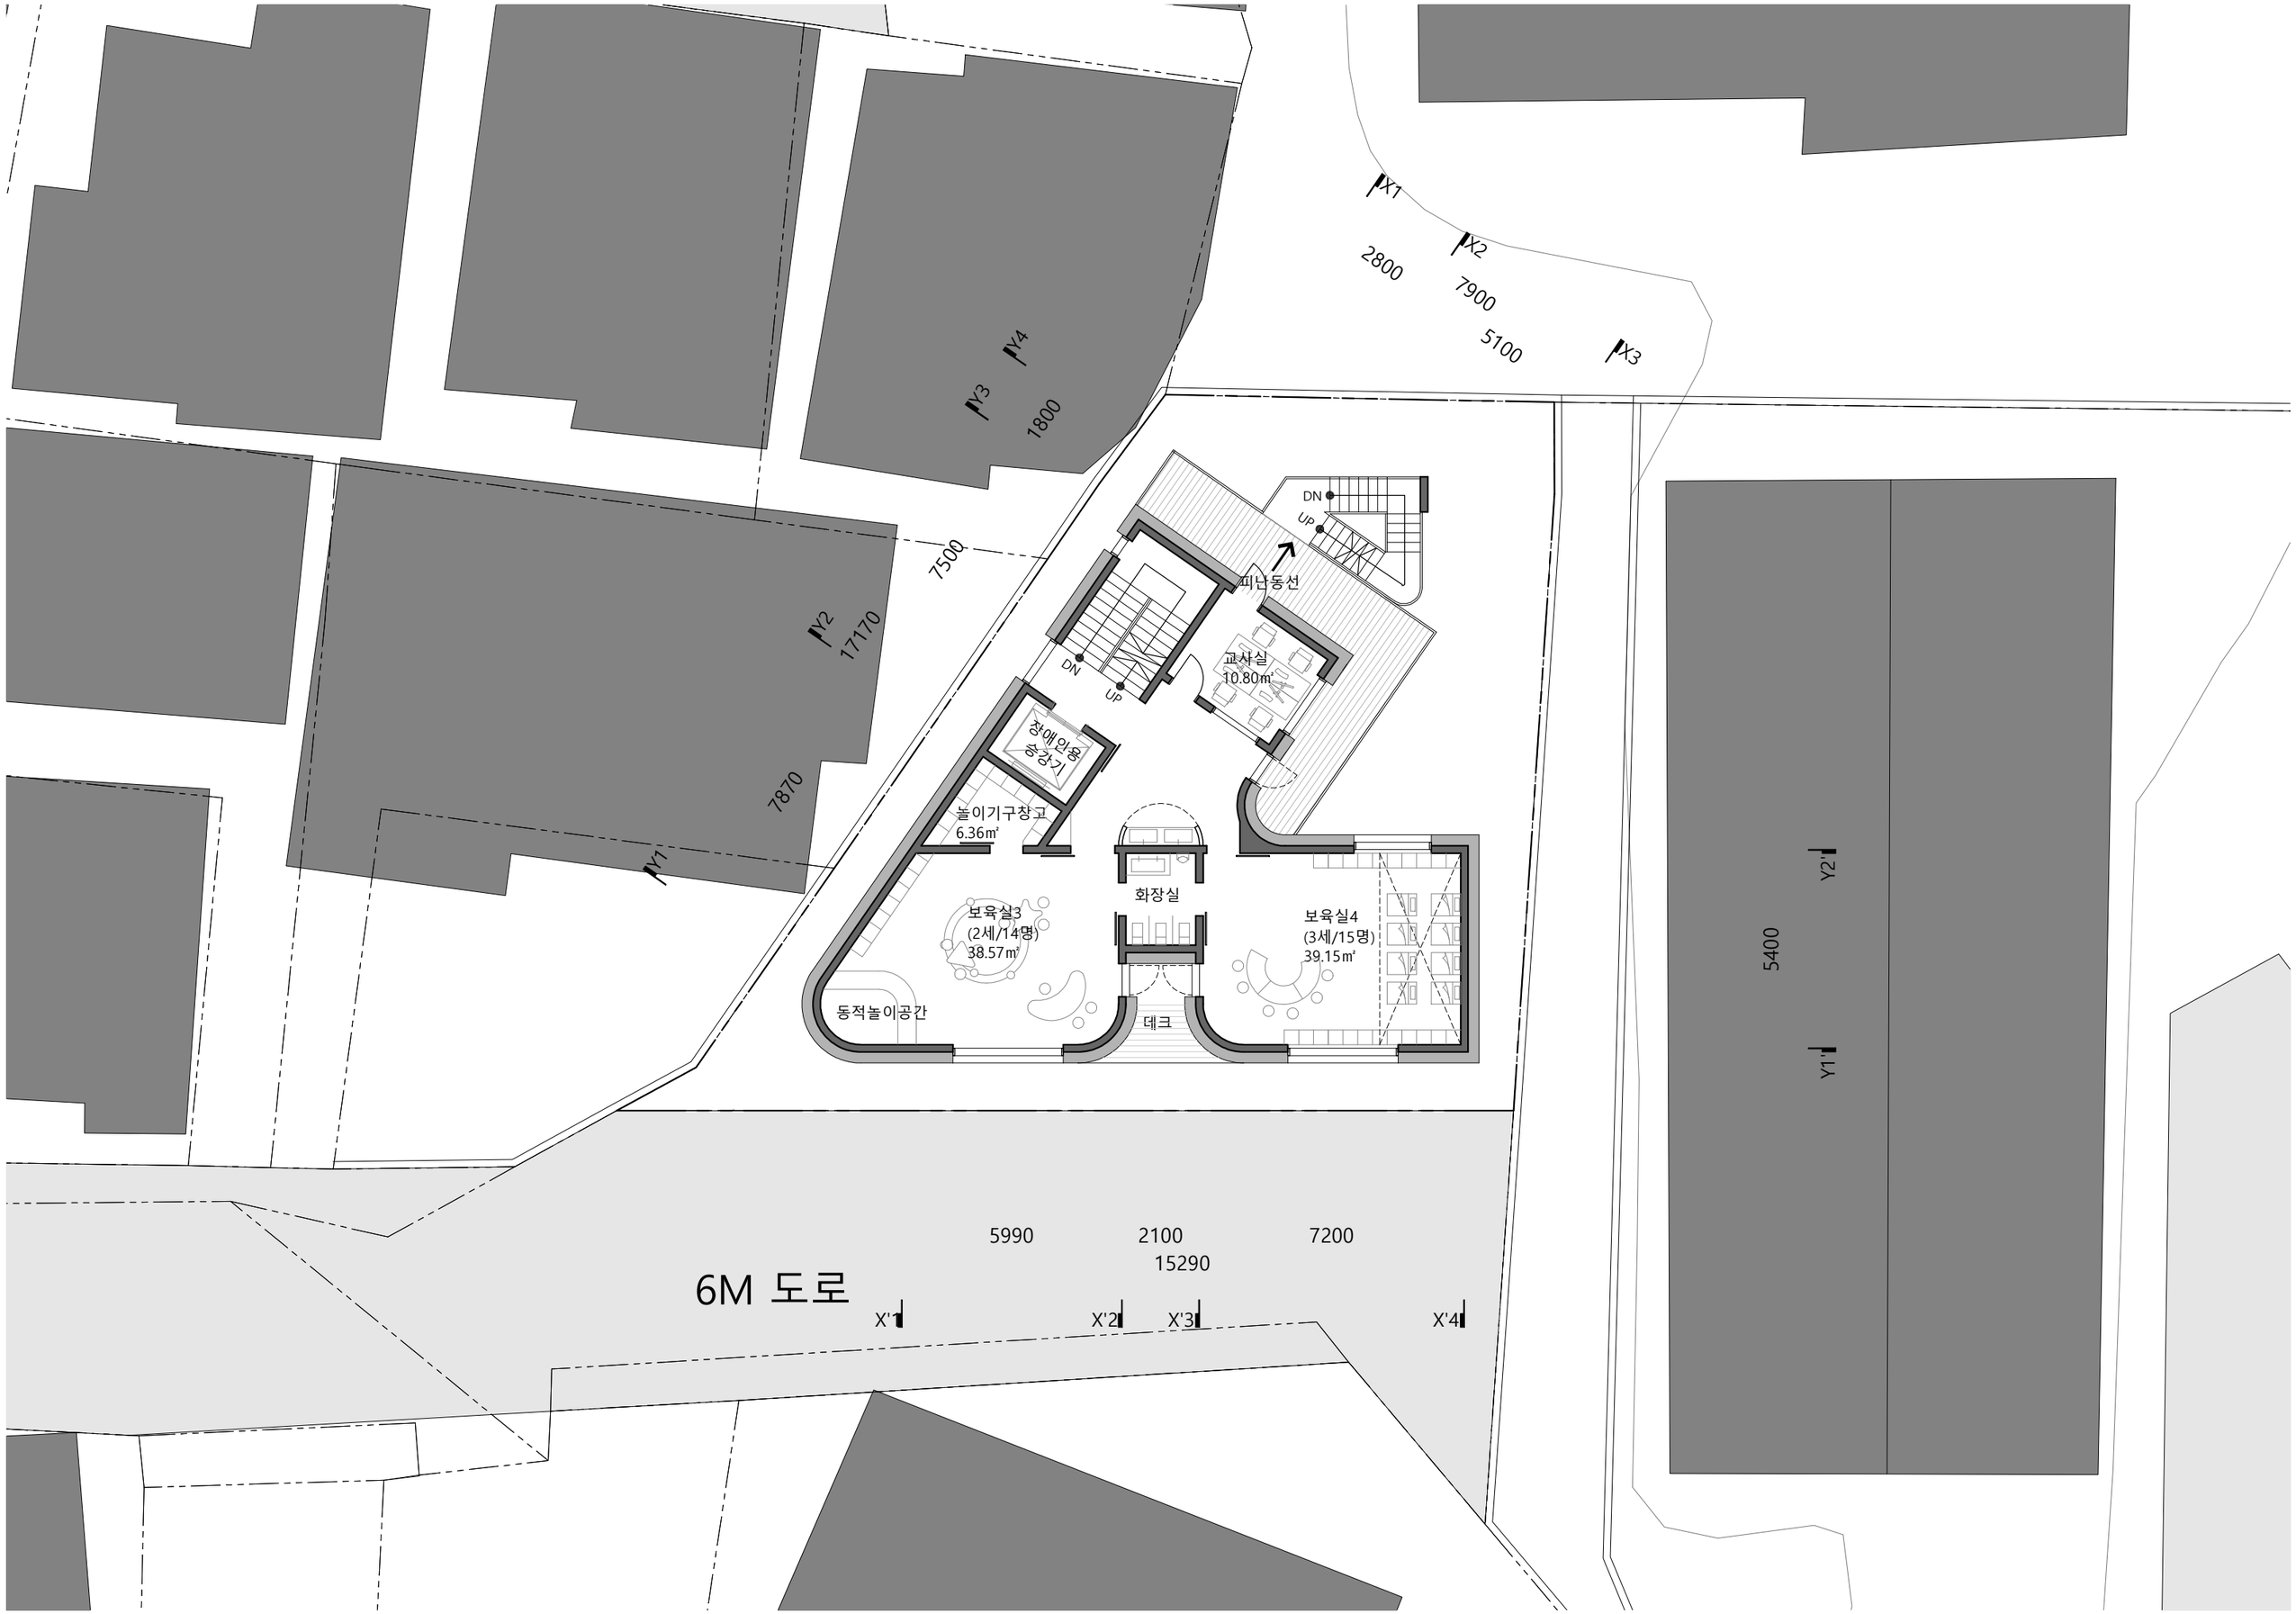

X1
X2
X3
2800
7900
5100
Y3
Y4
1800
7500
Y2
17170
7870
Y1
DN
UP
피난동선
교사실
10.80㎡
DN
UP
장애인용
승강기
놀이기구창고
6.36㎡
화장실
보육실3
(2세/14명)
38.57㎡
보육실4
(3세/15명)
39.15㎡
동적놀이공간
데크
5990
2100
7200
15290
6M 도로
X'1
X'2
X'3
X'4
Y2'
5400
Y1'