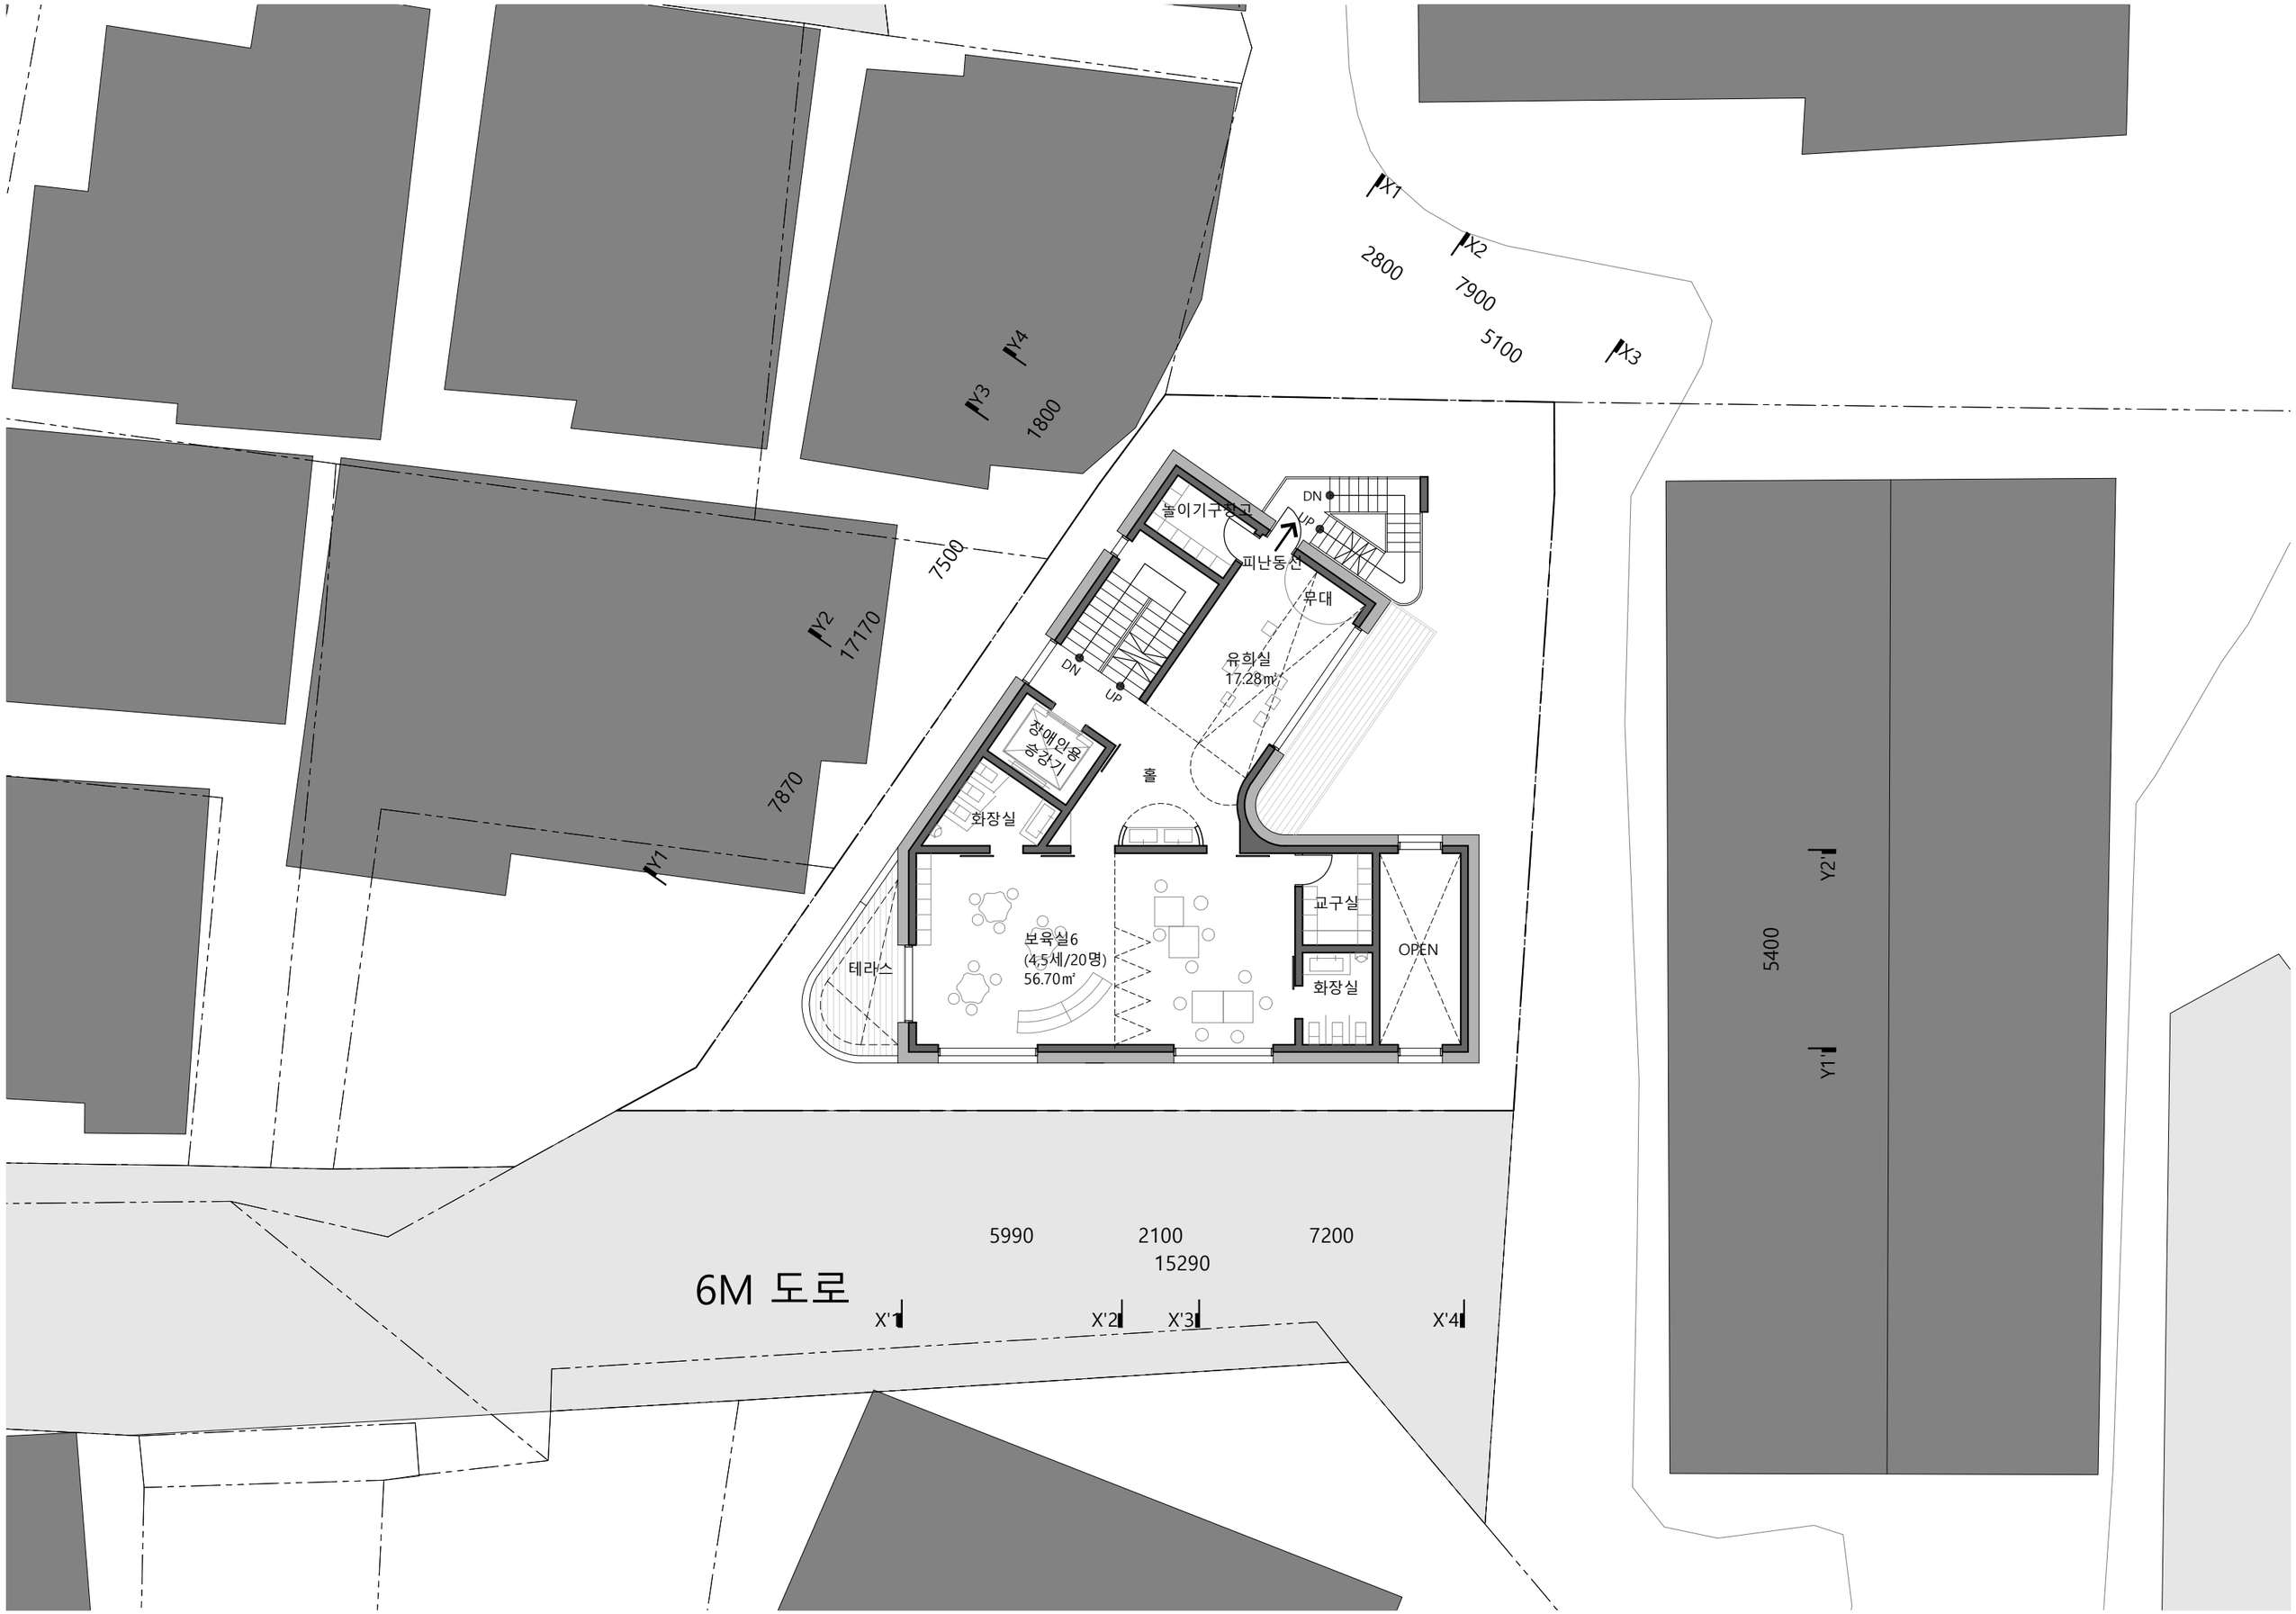

X1
X2
X3
2800
7900
5100
Y3
Y4
1800
Y2
17170
7500
7870
Y1
놀이기구창고
DN
UP
피난동선
무대
유희실
17.28㎡
DN
UP
장애인용
승강기
홀
화장실
보육실6
(4,5세/20명)
56.70㎡
테라스
교구실
OPEN
화장실
Y2'
Y1'
5400
5990
2100
7200
15290
6M 도로
X'1
X'2
X'3
X'4