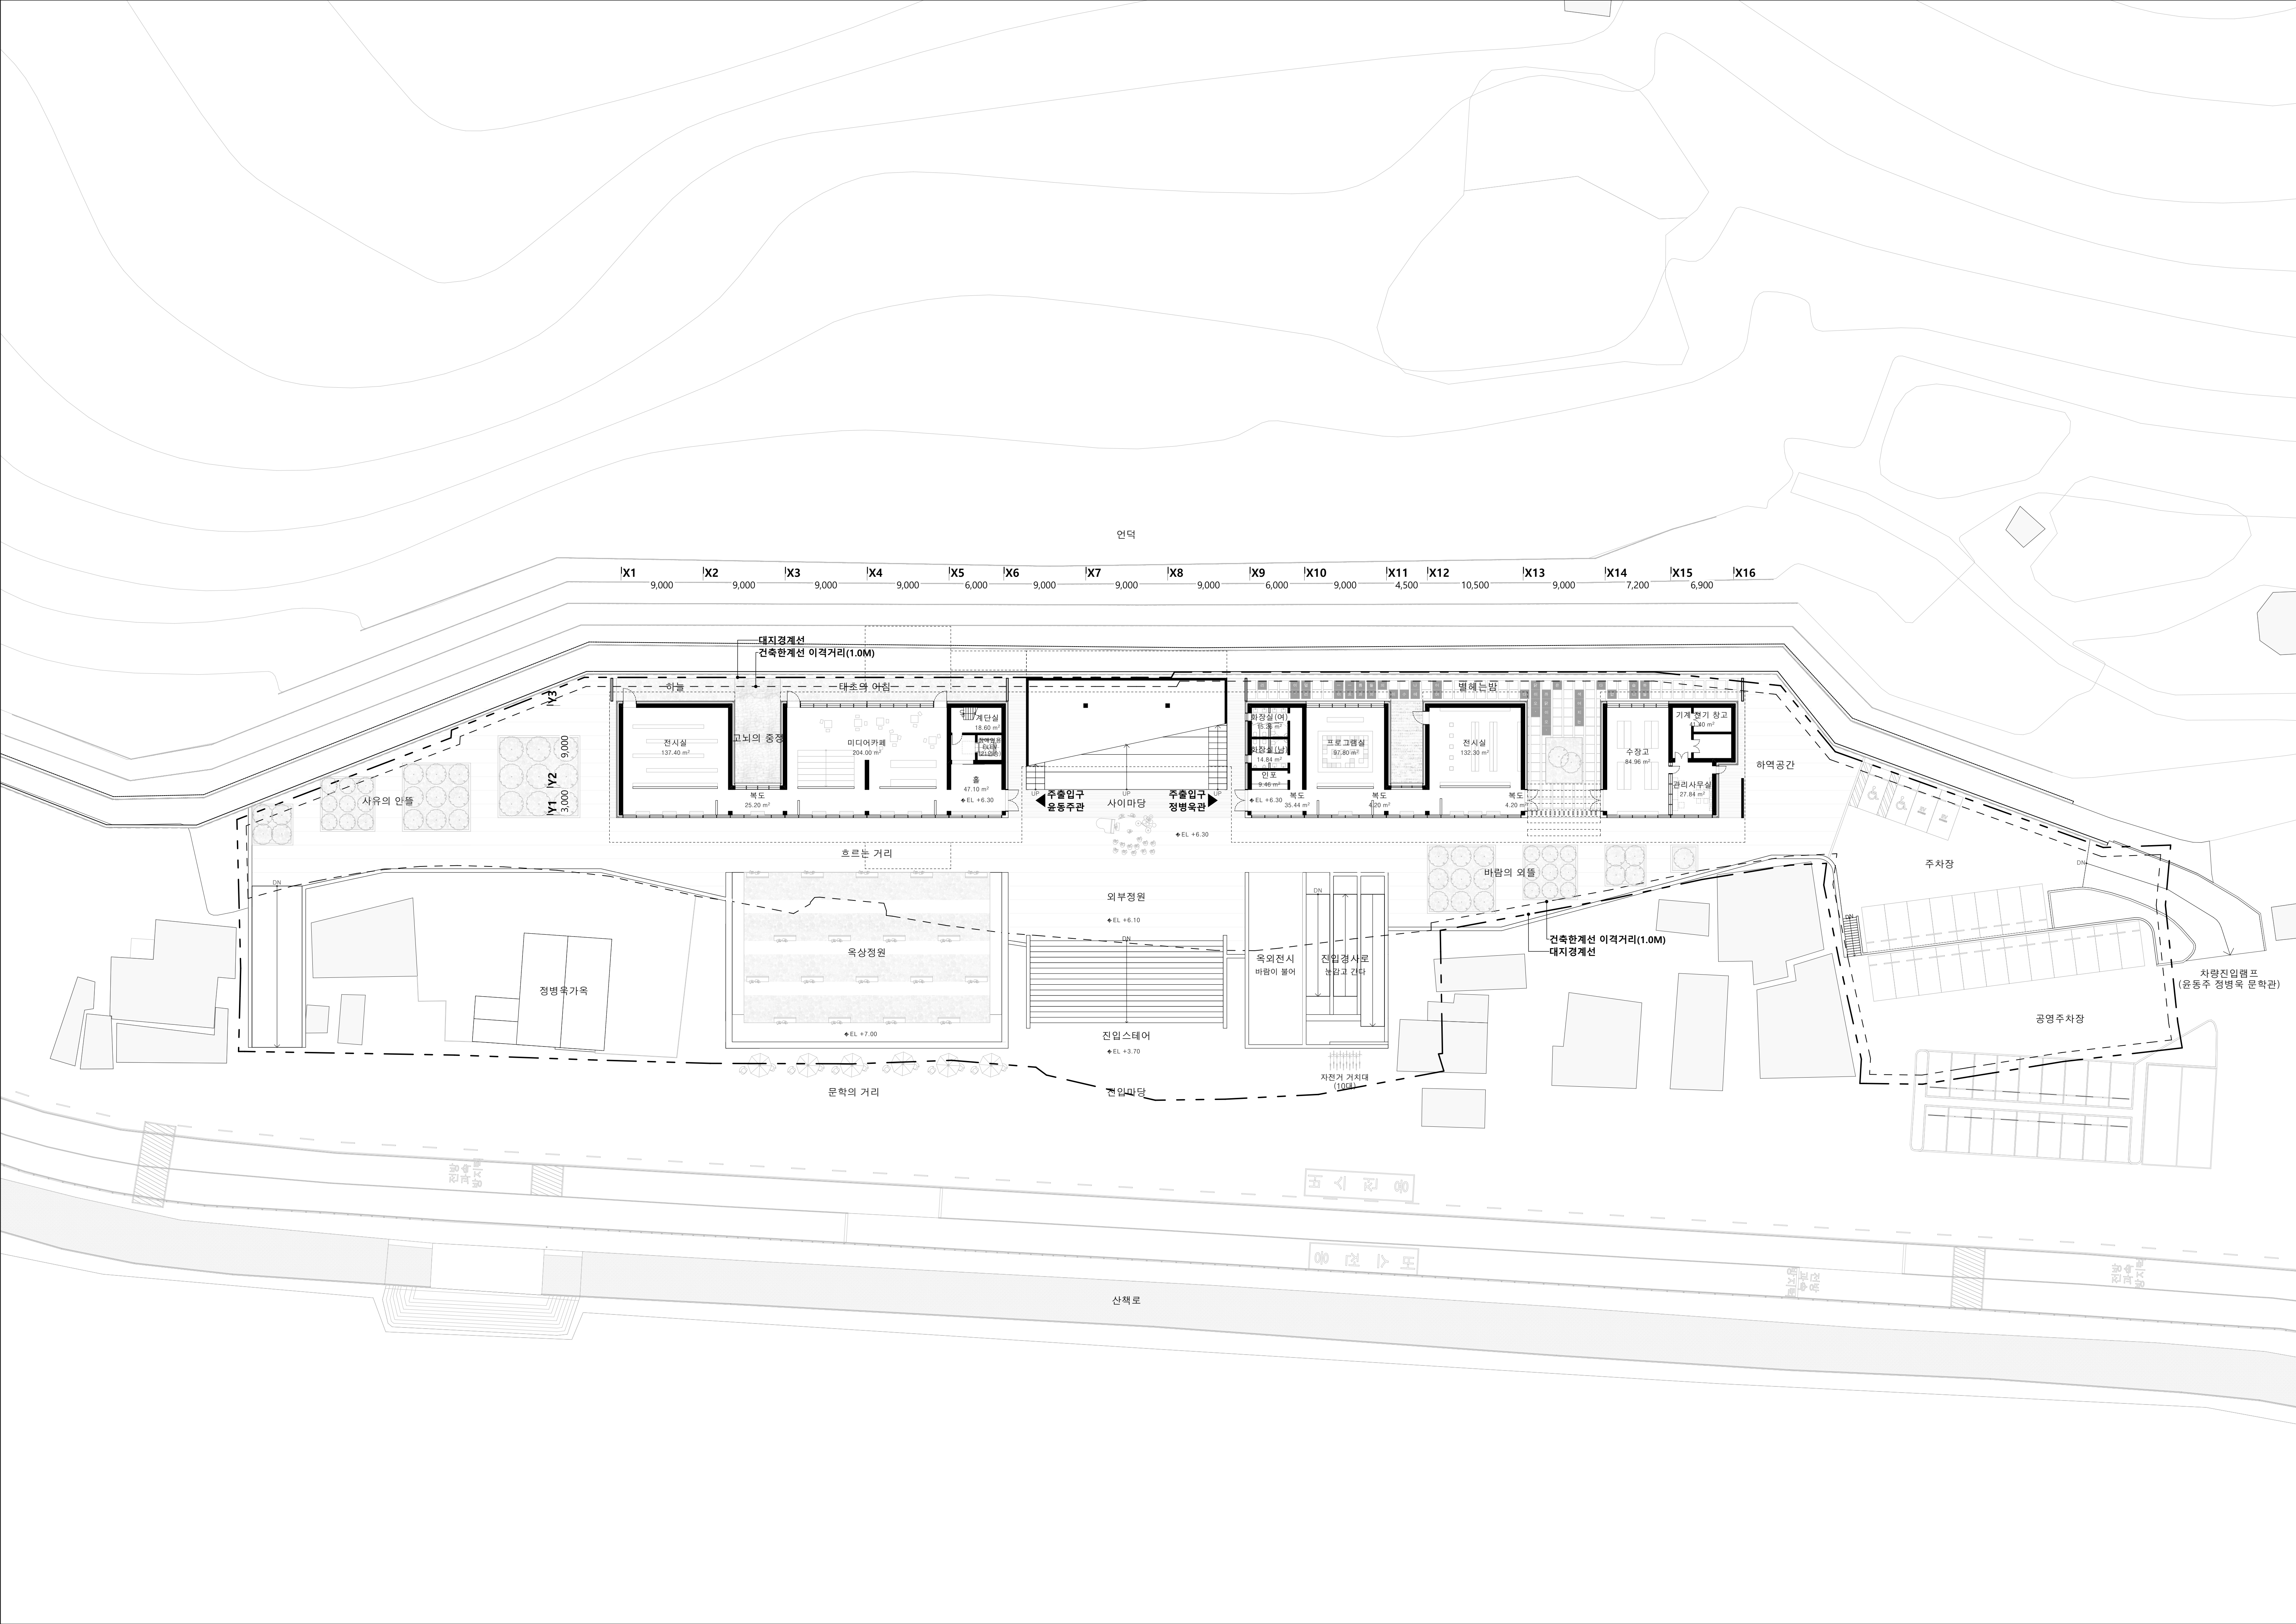
언덕
X1
X2
X3
X4
X5
X6
X7
X8
X9
X10
X11
X12
X13
X14
X15
X16
9,000
9,000
9,000
9,000
6,000
9,000
9,000
9,000
6,000
9,000
4,500
10,500
9,000
7,200
6,900
대지경계선
건축한계선 이격거리(1.0M)
Y3
Y2
Y1
9,000
3,000
하늘
태초의 아침
별헤는밤
사유의 안뜰
전시실
137.40 m²
고뇌의 중정
미디어카페
204.00 m²
계단실
18.60 m²
장애인용 ELEV (21인승)
홀
47.10 m²
♦EL +6.30
복도
25.20 m²
UP
주출입구
윤동주관
사이마당
주출입구
정병욱관
♦EL +6.30
화장실(여)
15.26 m²
화장실(남)
14.84 m²
인포
9.46 m²
♦EL +6.30
복도
35.44 m²
프로그램실
97.80 m²
복도
4.20 m²
전시실
132.30 m²
복도
4.20 m²
수장고
84.96 m²
기계 전기 창고
41.40 m²
관리사무실
27.84 m²
하역공간
흐르는 거리
바람의 외뜰
주차장
외부정원
♦EL +6.10
DN
옥상정원
♦EL +7.00
진입스테어
♦EL +3.70
옥외전시
바람이 불어
진입경사로
눈감고 간다
건축한계선 이격거리(1.0M)
대지경계선
차량진입램프
(윤동주 정병욱 문학관)
공영주차장
정병욱가옥
자전거 거치대
(10대)
문학의 거리
진입마당
산책로