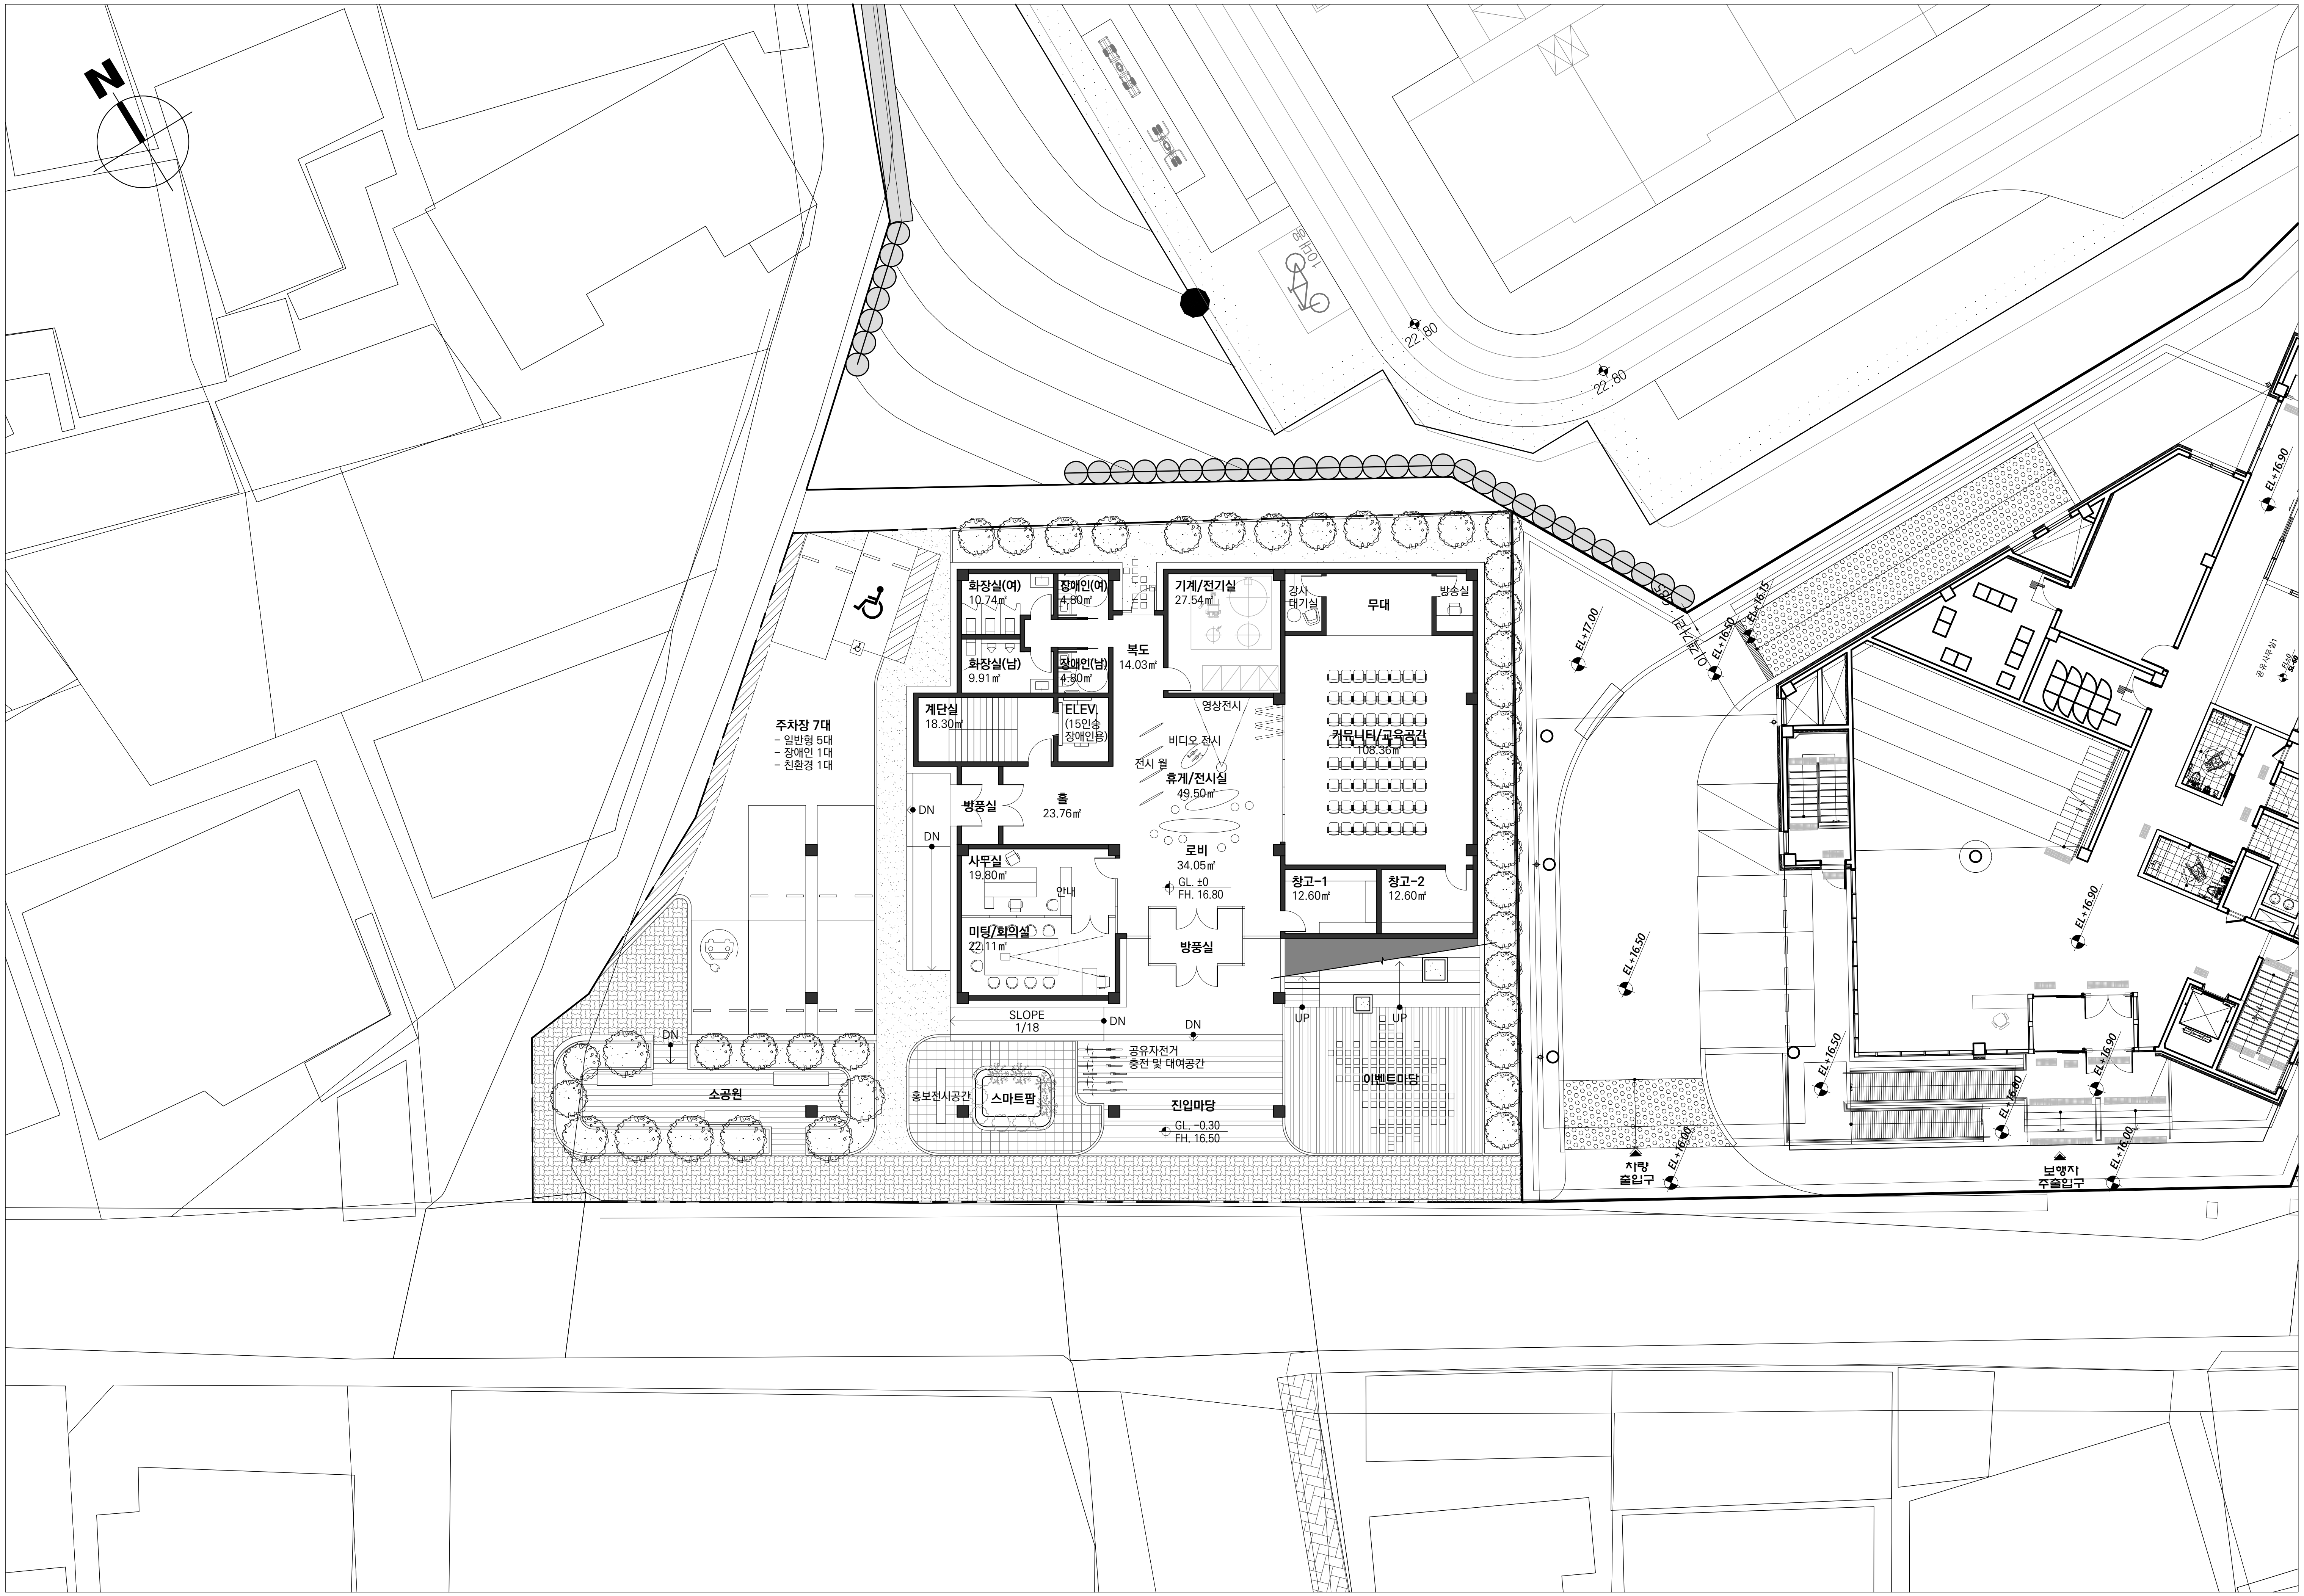
N
22.80
22.80
화장실(여)
10.74㎡
장애인(여)
4.80㎡
화장실(남)
9.91㎡
장애인(남)
4.80㎡
복도
14.03㎡
기계/전기실
27.54㎡
강사
대기실
무대
방송실
계단실
18.30㎡
ELEV.
(15인승
장애인용)
영상전시
비디오 전시
전시 월
휴게/전시실
49.50㎡
커뮤니티/교육공간
108.36㎡
방풍실
홀
23.76㎡
로비
34.05㎡
GL. ±0
FH. 16.80
사무실
19.80㎡
안내
창고-1
12.60㎡
창고-2
12.60㎡
미팅/회의실
22.11㎡
방풍실
DN
DN
SLOPE
1/18
DN
DN
UP
UP
주차장 7대
- 일반형 5대
- 장애인 1대
- 친환경 1대
소공원
DN
공유자전거
충전 및 대여공간
홍보전시공간
스마트팜
진입마당
GL. -0.30
FH. 16.50
이벤트마당
EL+17.00
EL+16.50
EL+16.15
EL+16.50
EL+16.90
EL+16.90
EL+16.50
EL+16.90
EL+16.00
EL+16.00
EL+16.00
공유사무실1
EL±0
SL-60
차량
출입구
보행자
주출입구